
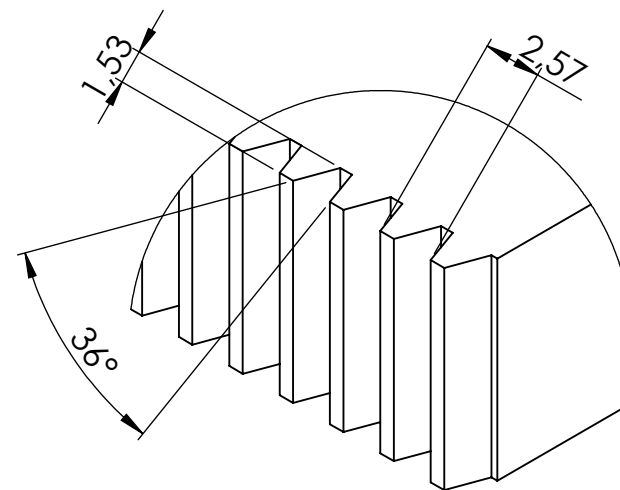
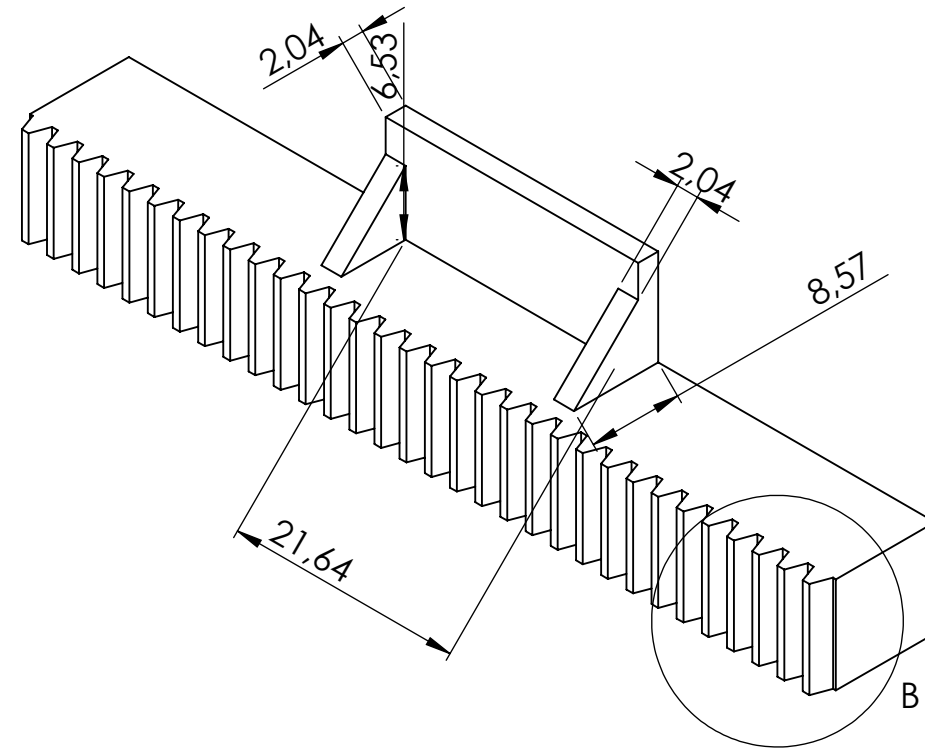


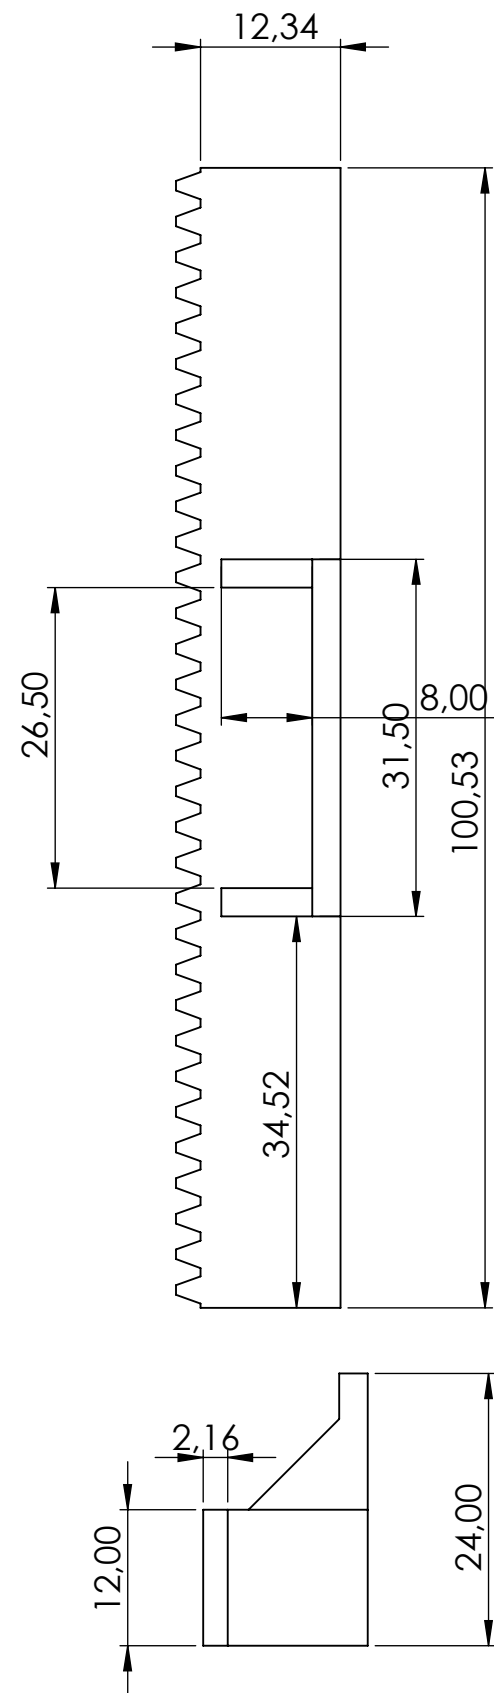

Section B